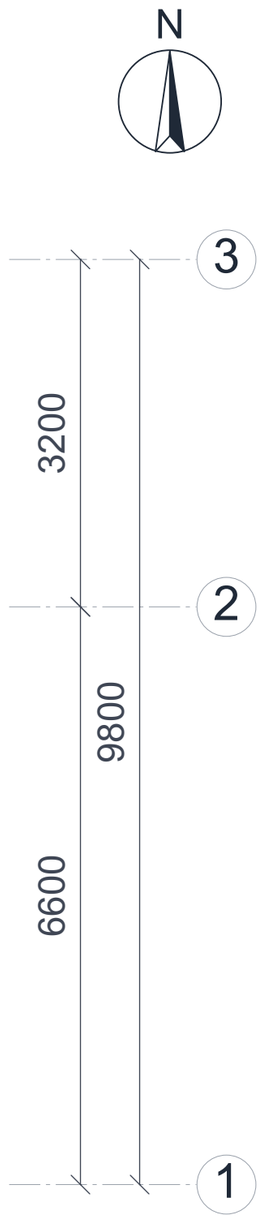

A B C D

Villa Riverside - Floor Plan.dwg

Scale 1:50 · A3 · mm
MD CAD AI STUDIO · 2026-10-18

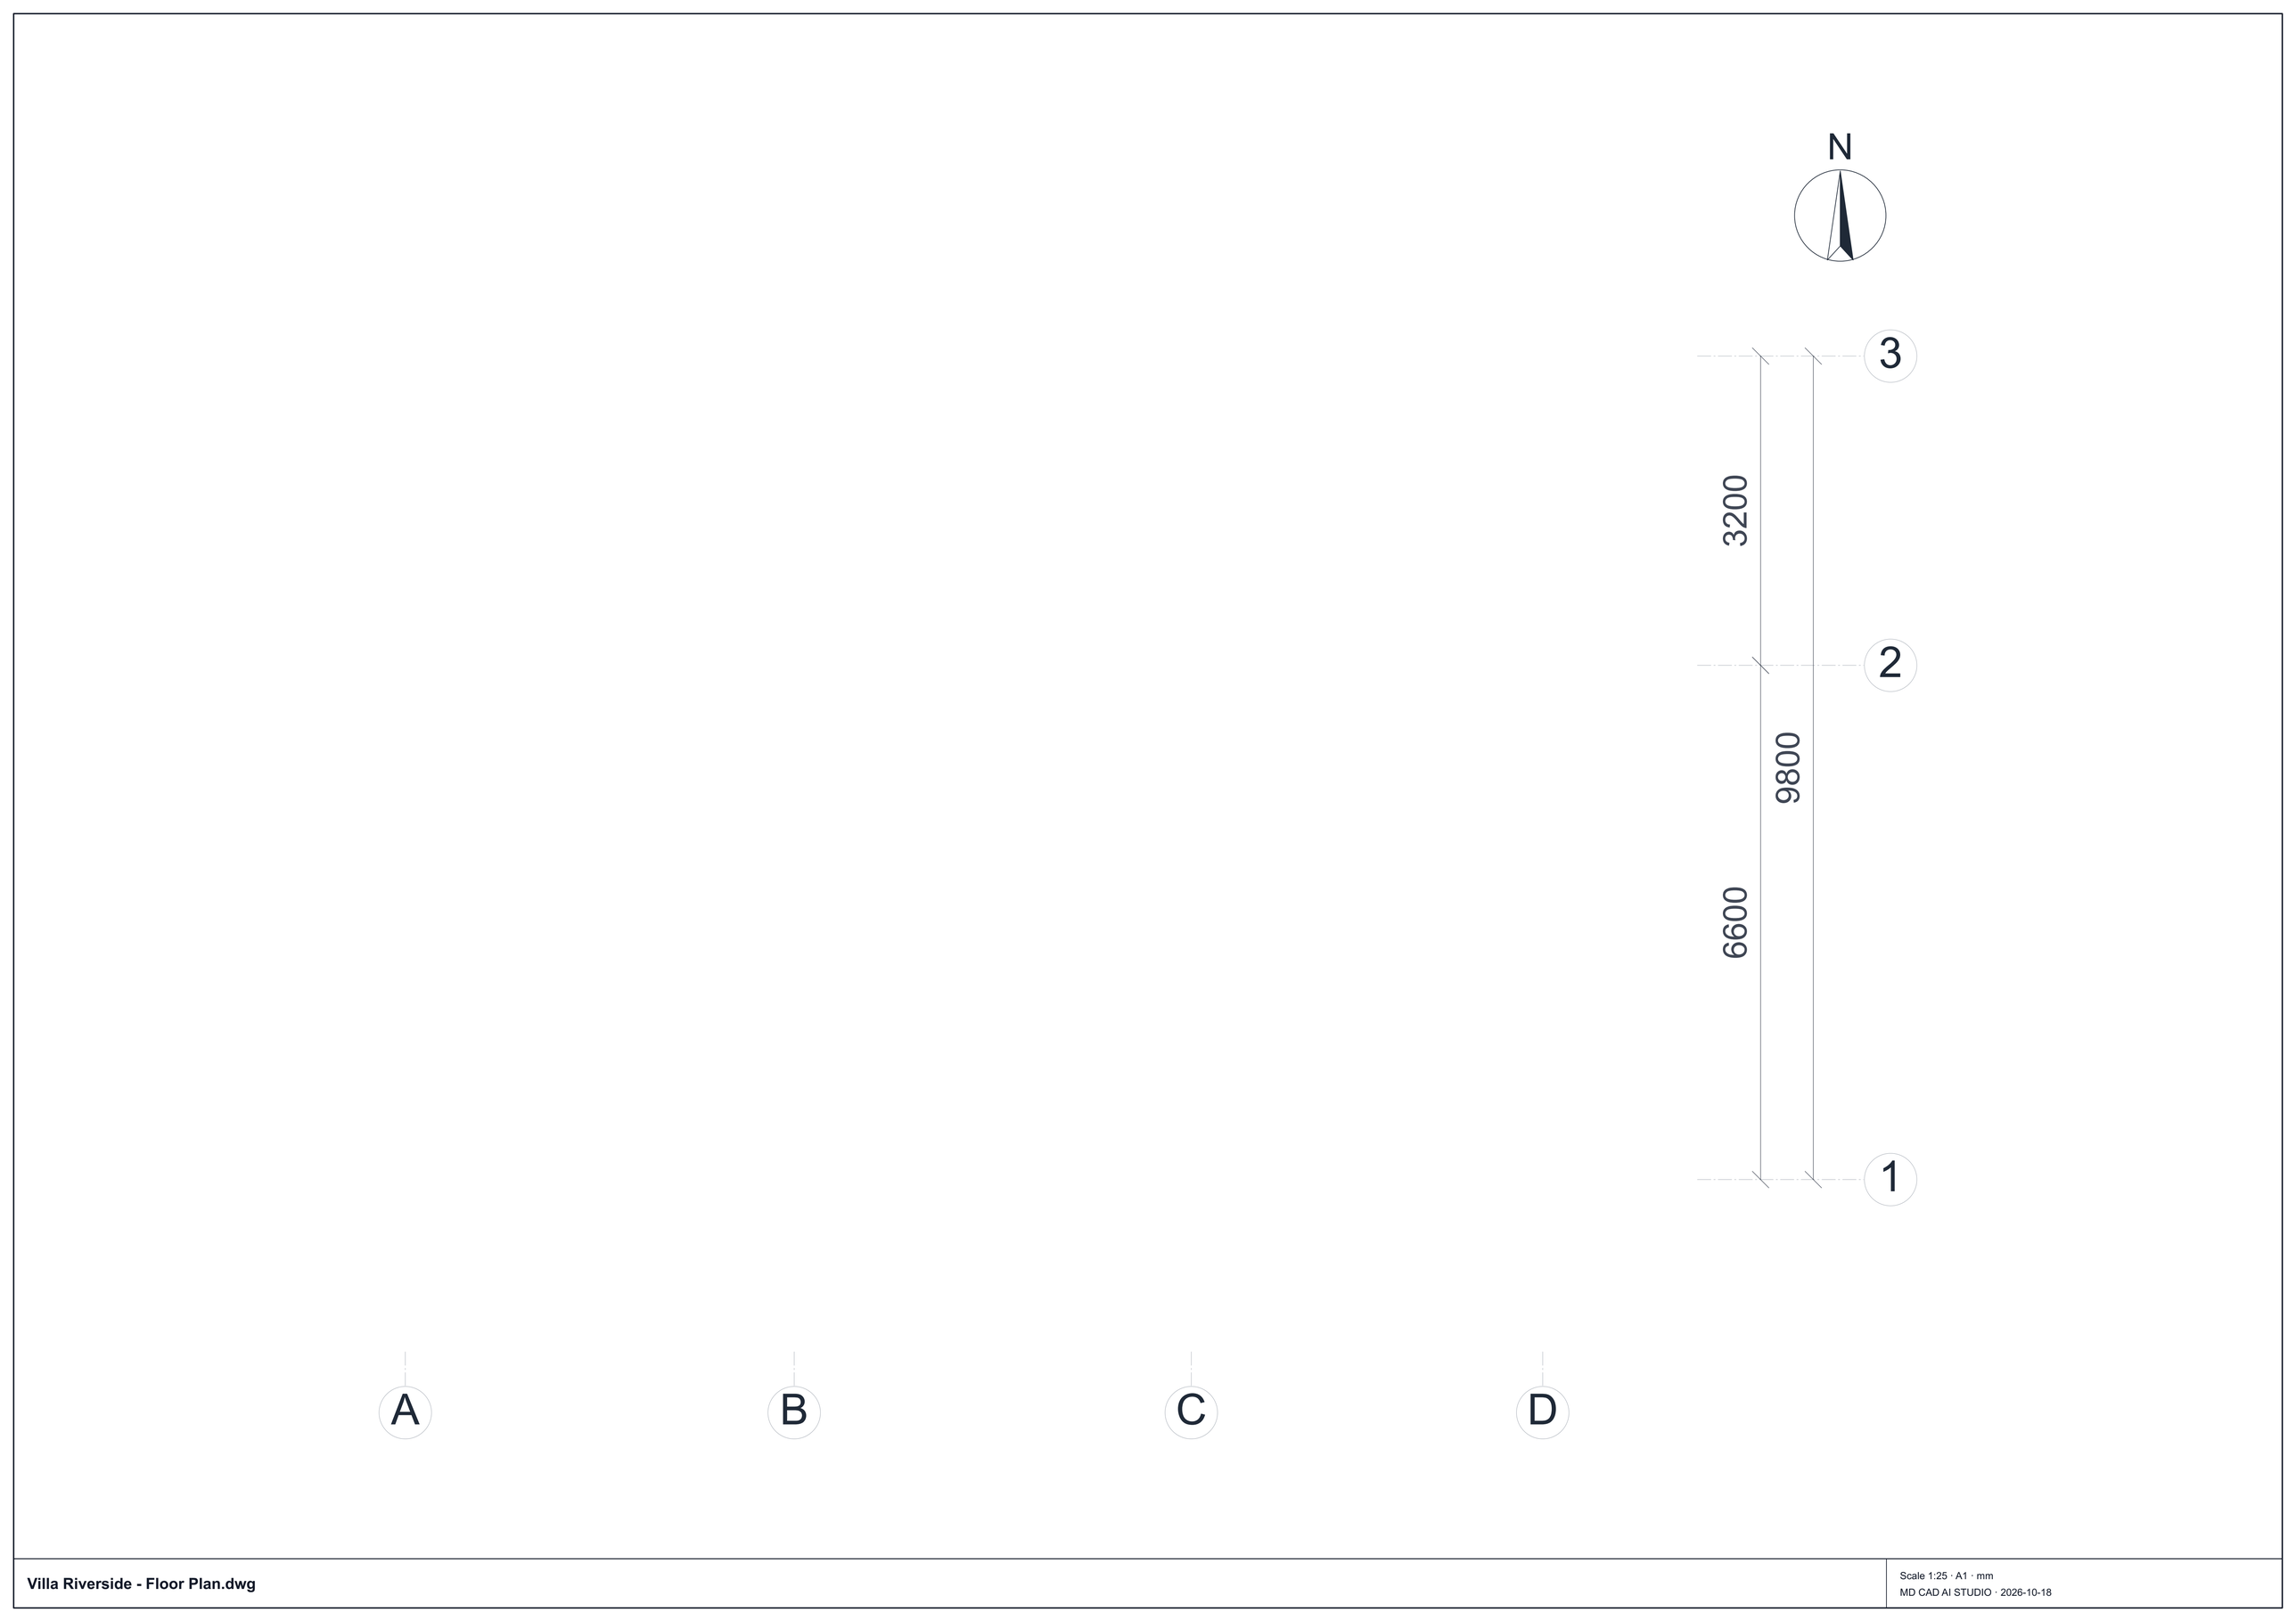

Villa Riverside - Floor Plan.dwg

Scale 1:25 · A1 · mm
MD CAD AI STUDIO · 2026-10-18

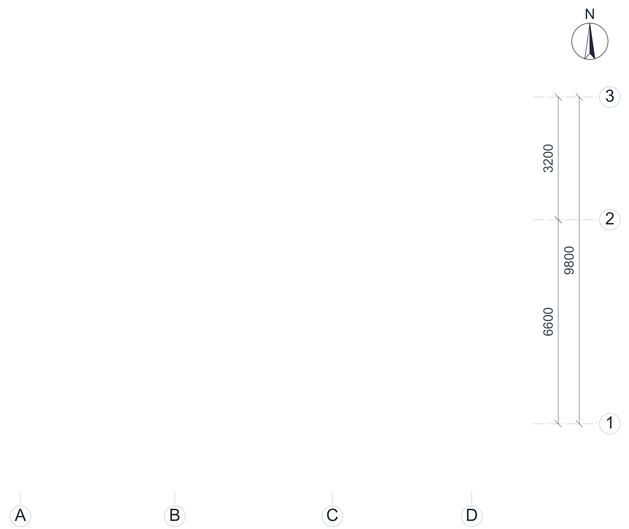

100 mm (paper) 1 m (model, 1:50)

Villa Riverside - Floor Plan.dwg

Scale 1:50 · A0 · mm
MD CAD AI STUDIO · 2026-10-18

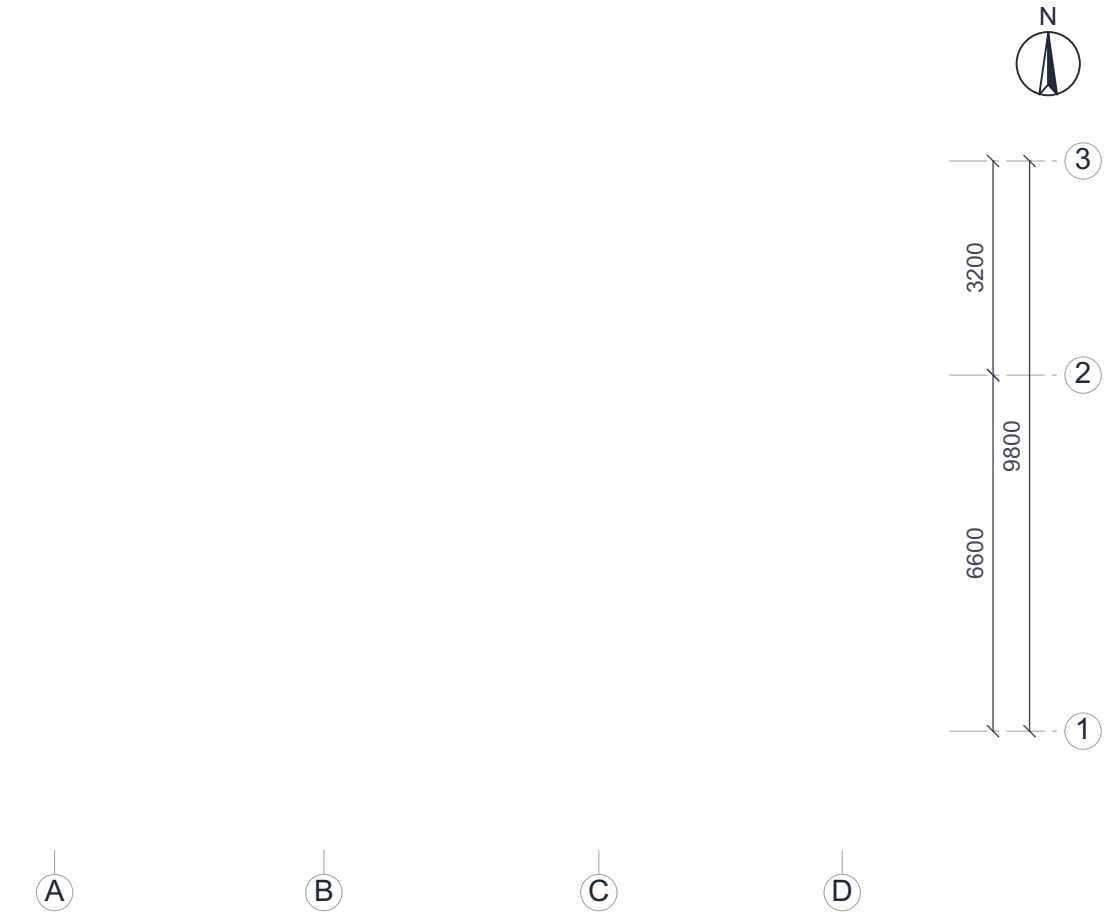

100 mm (paper)

1 m (model, 1:100)

Villa Riverside - Floor Plan.dwg

Scale 1:100 · A4 · mm

MD CAD AI STUDIO · 2026-10-18